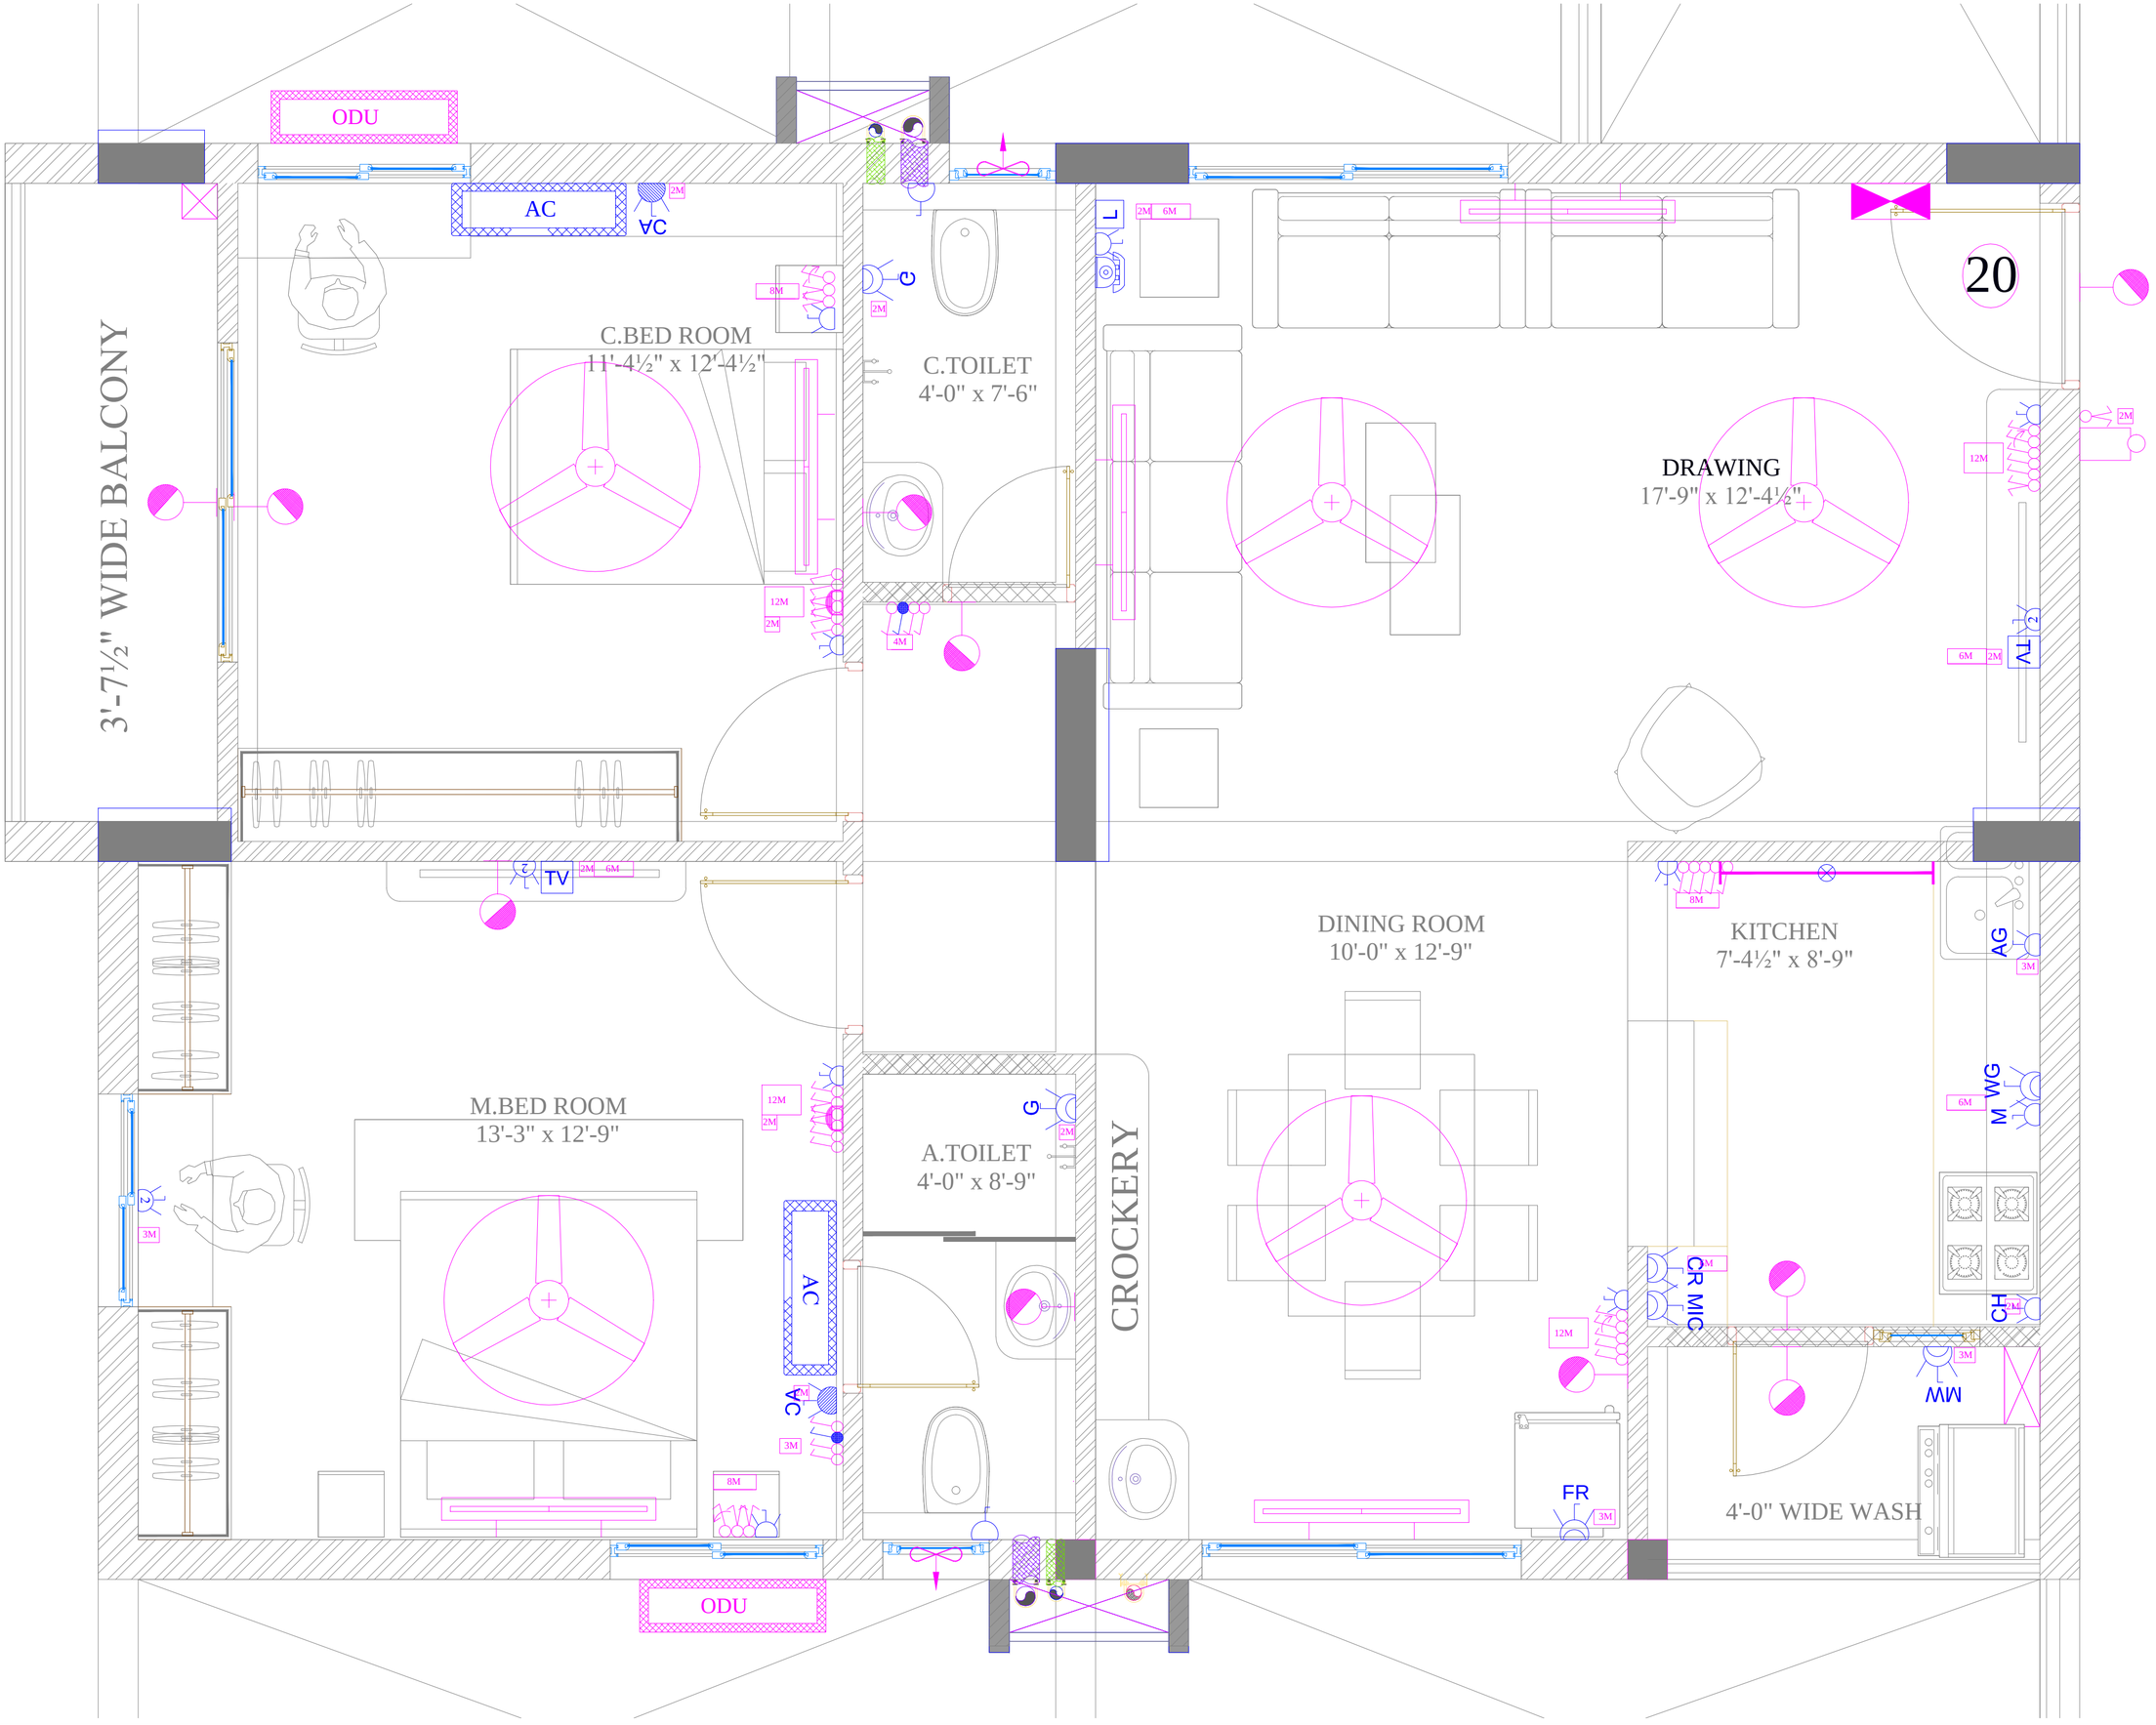


ARCHITECT

instone
ARCHITECTS & INTERIOR DESIGNERS
#First Floor, Plot No 258, Road No-78,
Prashashan Nagar, Jubilee Hills, Hyderabad-500033.
Ph-040-23310971; MOB-9966640971.
e-mail: info@instonearchitects.com
www.instonearchitects.com

NORTH

| | |
|---|---|
| DATE | 28-01-2019 |
| SCALE | NOT TO SCALE |
| DRAWN.BY | |
| CHEKD.BY | ANURADHA |
| APPR.BY | RAMANA REDDY |
| DWG NO:- | |

DWG TITLE: TYPICAL FLOOR PLAN

PROJECT: PROPOSED APARTMENT AT KOKAPET

CLIENT: M/S. HIRIZE CONSTRUCTIONS

| | |
|---|---|
| Date | : 02.01.2020 |
| SCALE | : N.T.S |
| Drawn : | |
| Checked : Vekateshwar Rao | |
| Approved : S PRASAD | |
| TYPICAL FLOOR FLAT-20 CONDUIT LAYOUT | |

MEP :
SPRASAD & ASSOCIATES
Sree Lakshmi Residency Flat :102
Chandanagar Hyderabad-500050
email: sprasad.135@gmail.com
Mobile:9959992858